


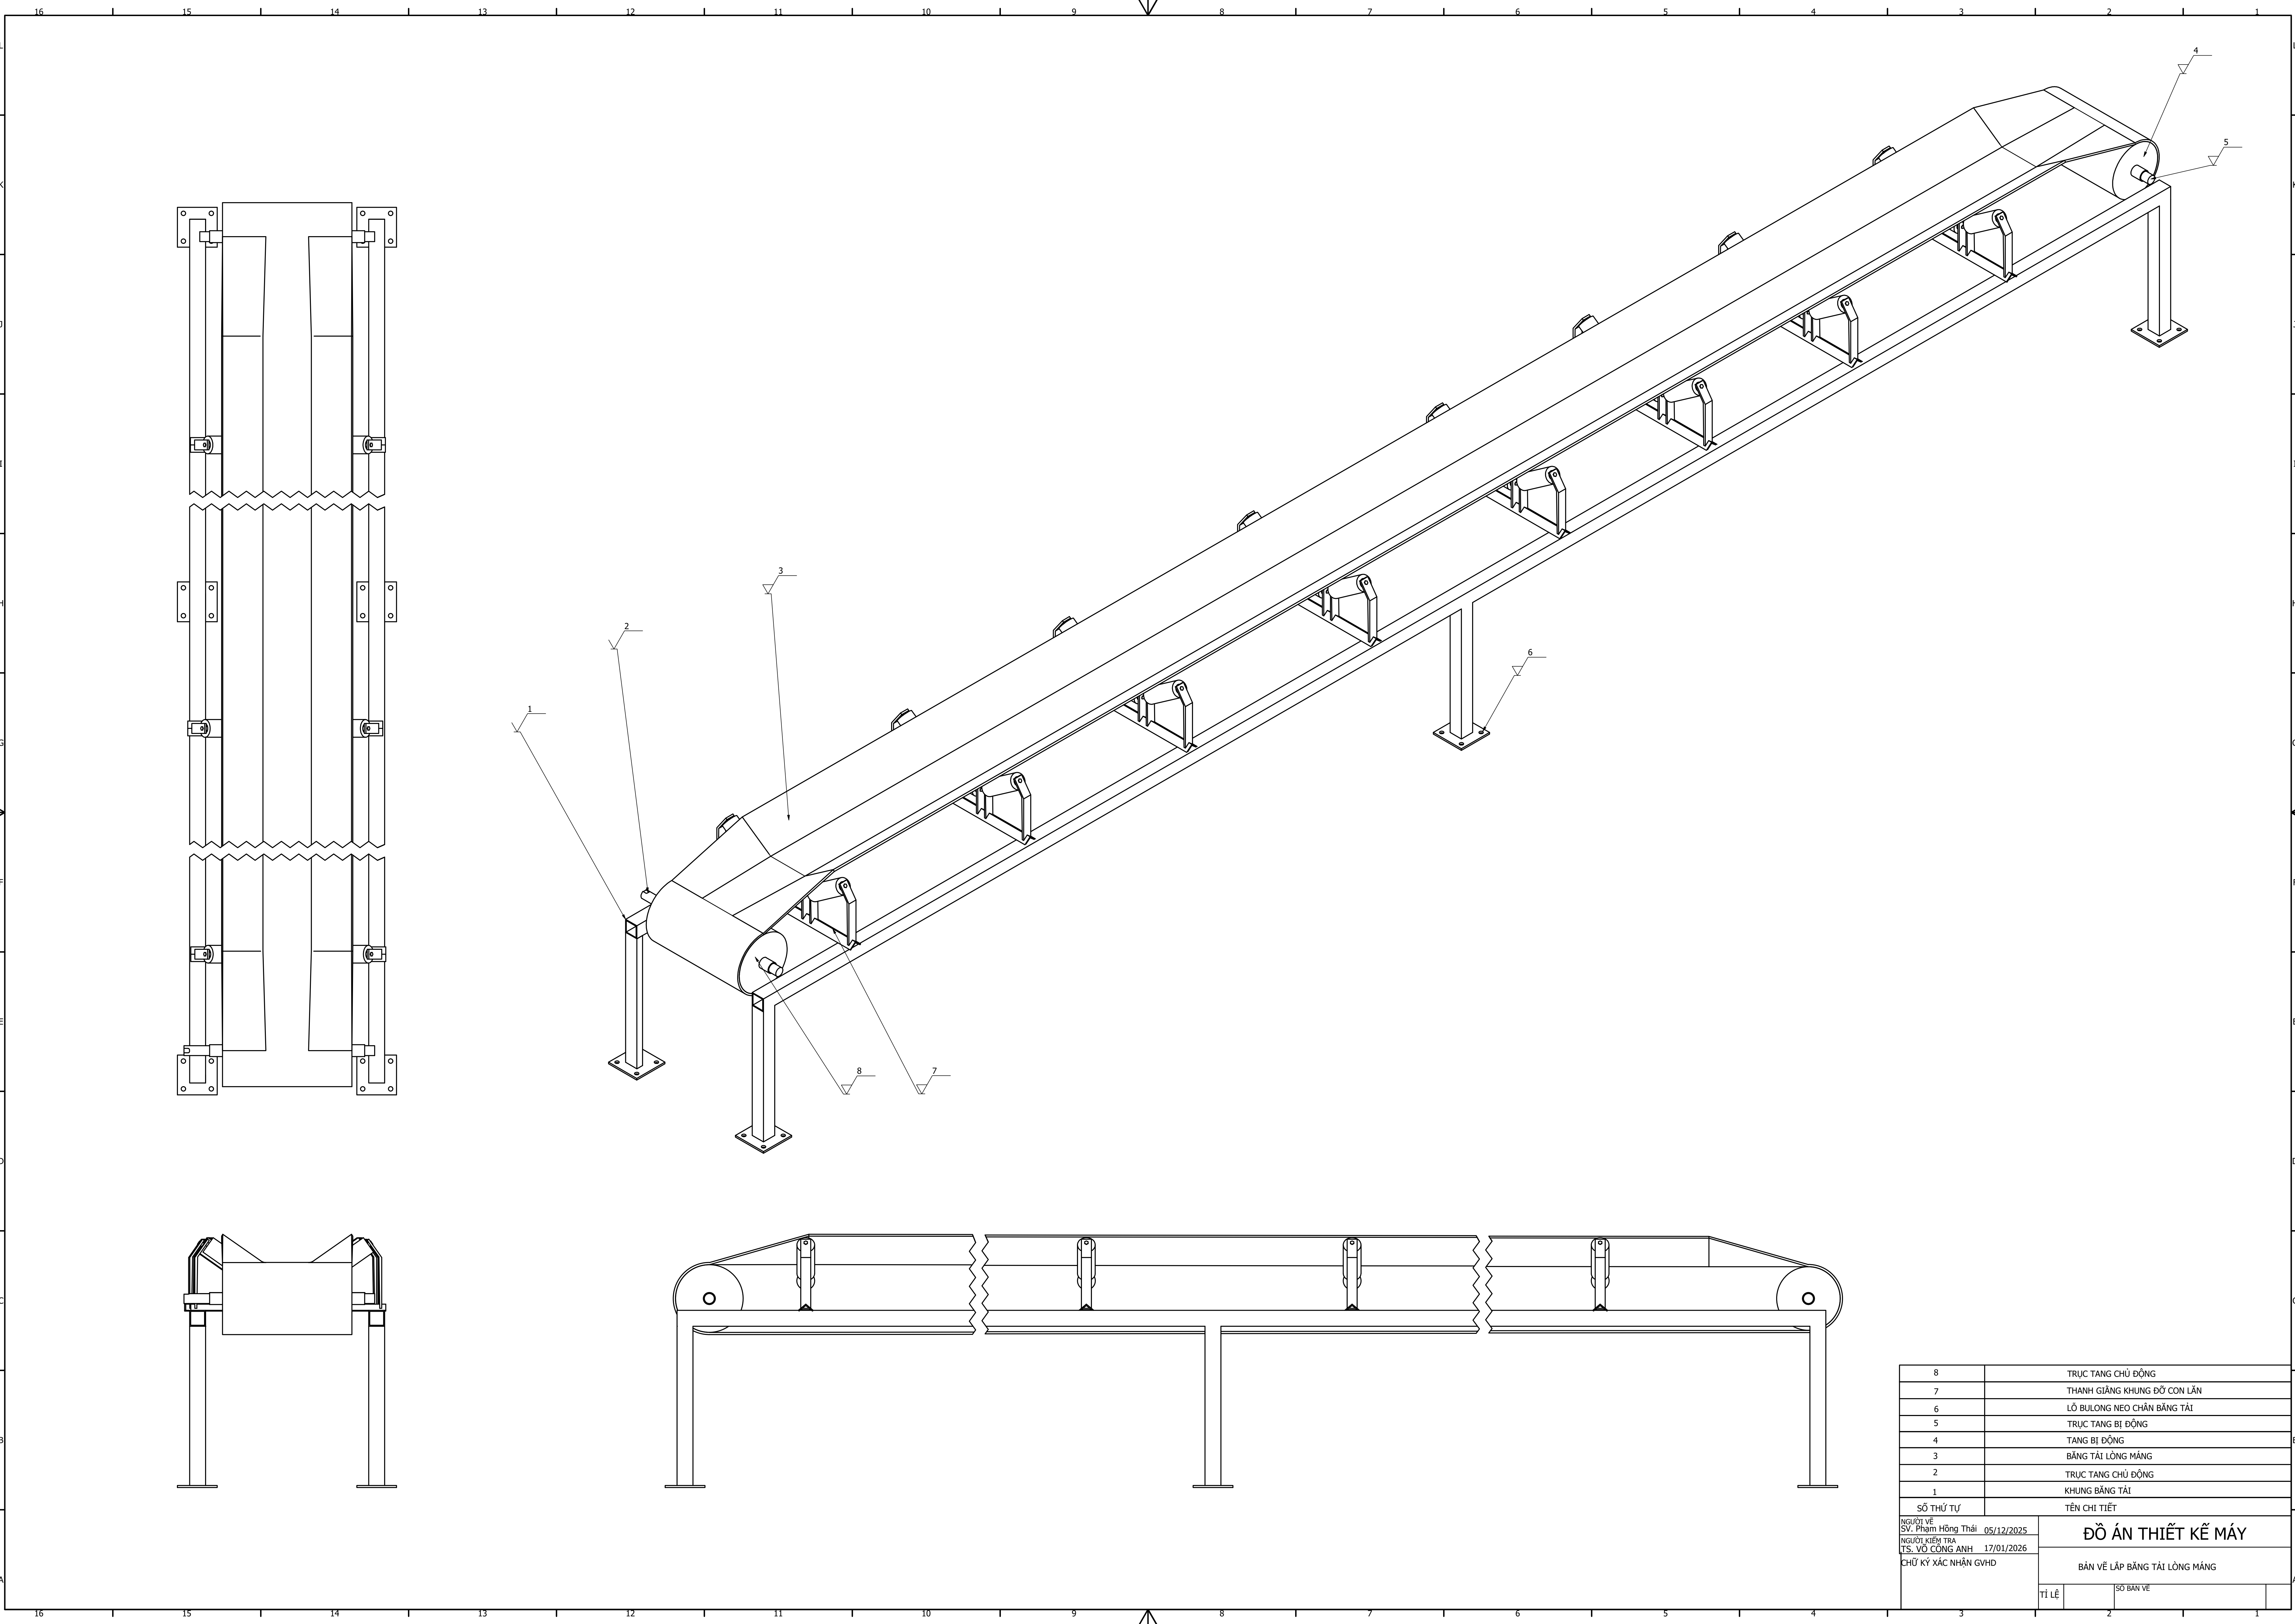

8	TRỤC TANG CHỦ ĐỘNG	
7	THANH GIÀNG KHUNG ĐỖ CON LĂN	
6	LỖ BULÔNG NEO CHÂN BẢNG TẢI	
5	TRỤC TANG BỊ ĐỘNG	
4	TANG BỊ ĐỘNG	
3	BẢNG TẢI LÔNG MĂNG	
2	TRỤC TANG CHỦ ĐỘNG	
1	KHUNG BẢNG TẢI	
SỐ THỨ TỰ	TÊN CHI TIẾT	
NGƯỜI VẼ SV. Phạm Hồng Thái 05/12/2025 NGƯỜI KIỂM TRA TS. VŨ CÔNG ANH 17/01/2026 CHỮ KÝ XÁC NHẬN GVHD ĐỒ ÁN THIẾT KẾ MÁY BẢN VẼ LẬP BẢNG TẢI LÔNG MĂNG TỈ LỆ SỐ BẢN VẼ		